


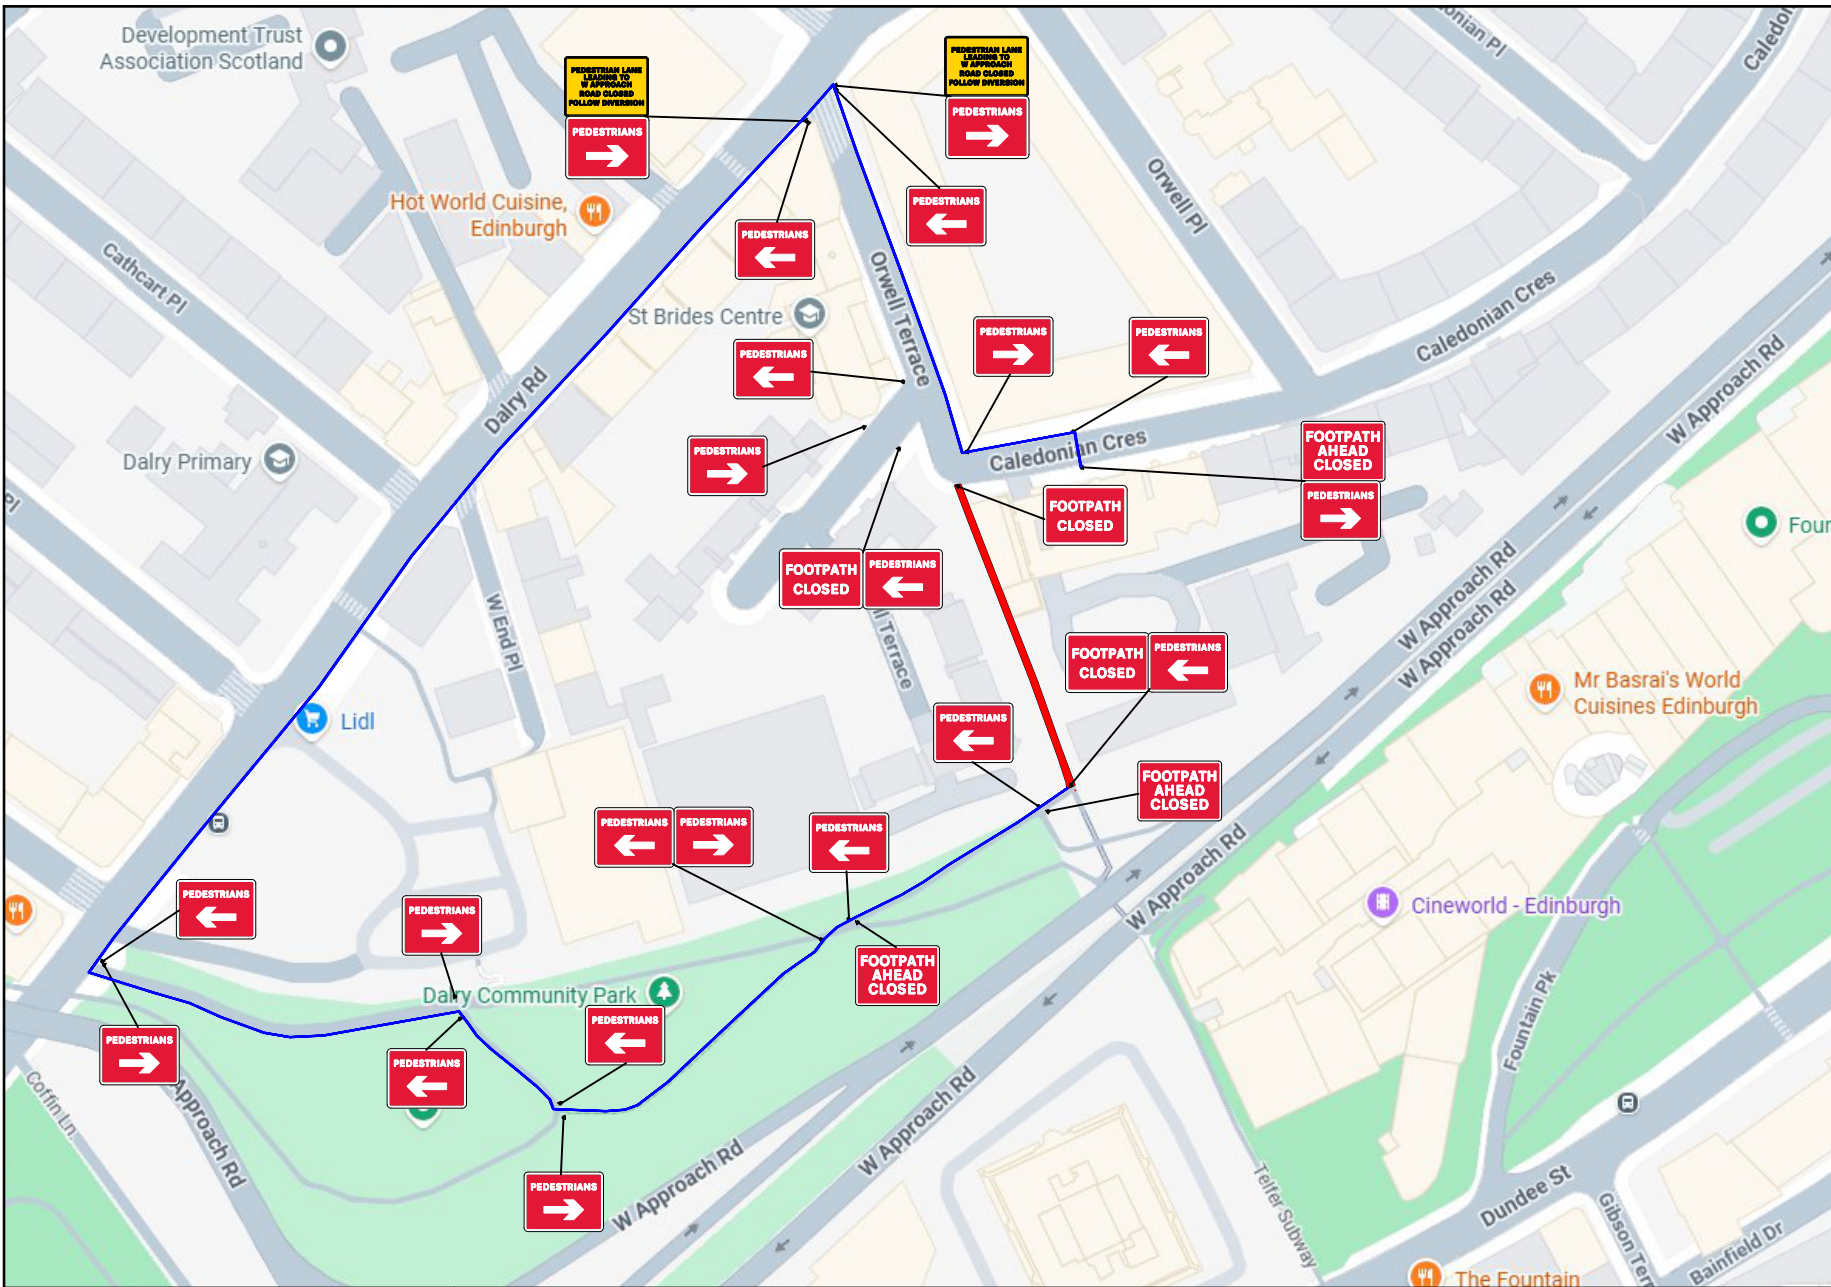

Site Address: Caledonian Crescent Edinburgh	
Client: E.C.C	
Maclay Contact: Airdrie Office	
Date of works: T.B.A	
Drawn by: TK	Date drawn: X
Drawing Requested By: E.C.C	
KEY — Diversion Route ● 750 Road Cones ● Sign → Temporary Pedestrian Crossing ⚡ Temporary Traffic Signals ⚡ Footpath Works Area ⚡ Safety Zone ⚡ Bus Stop To Be Suspended ⊕ Stop & Go ⚡ Pedestrian Barrier	
Drawing Number: TK/	

NOTES

1) All temporary traffic management shall be in accordance with Chapter 8 Part 1 Design (2009); Part 2 Operations (2009); Part 3 Update (2020).

2) All temporary traffic management shall be in accordance with the Traffic Signs Regulations and General Directions 2016.

3) All temporary traffic management shall conform to the Safety at Streetworks and Road Works ACOP 2013.

4) All temporary traffic management signs should be located 450mm minimum from the kerb face.

5) All temporary traffic management sign locations are indicative and are subject to on site approval from the supervisor.

PEDESTRIAN LANE DIVERSION

SET-UP TO BE IN ACCORDANCE WITH THE NRSWA SAFETY AT STREET WORKS CODE

38 Stirling Road,
Airdrie,
ML6 7JA
Tel: 01236 768388
E-mail: tkiddle@maclaycivil.co.uk